R:\sh\F\FE-sheets\A1800.dgn

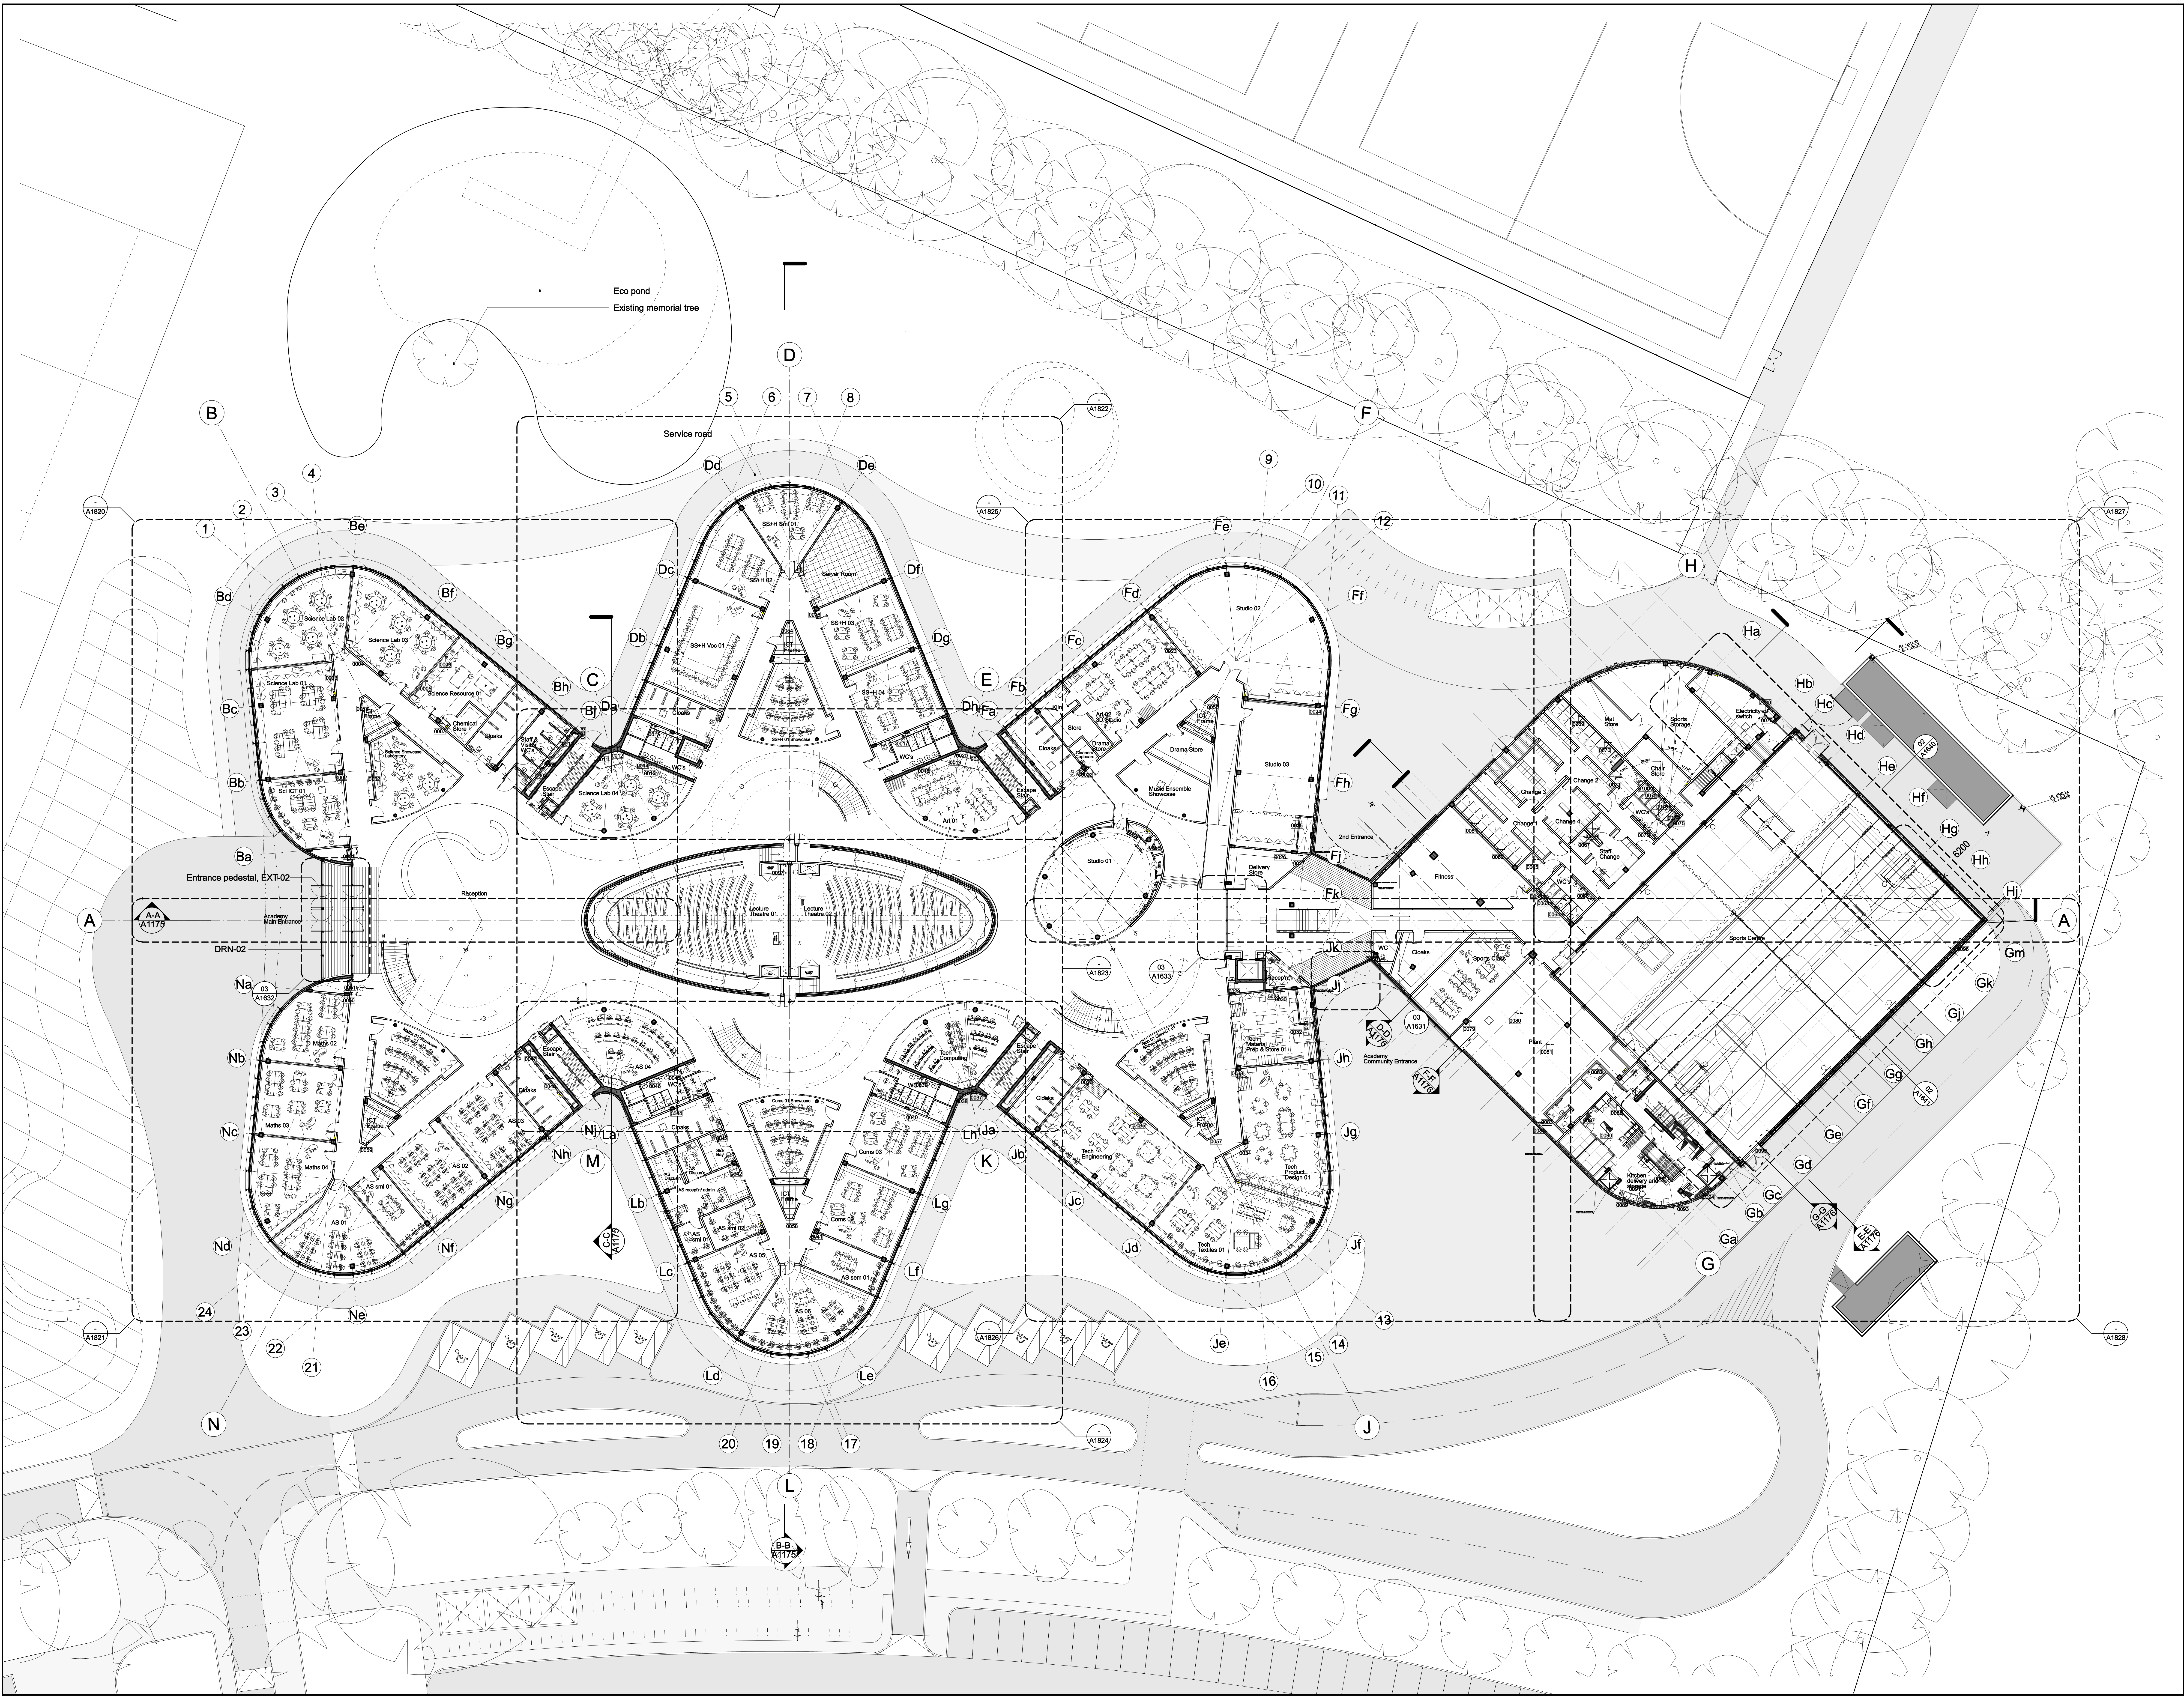
Eco pond
Existing memorial tree
Service road
Entrance pedestal, EXT-02
Academy Main Entrance
DRN-02
Reception
Science Lab 01
Science Lab 02
Science Lab 03
Science Lab 04
Science Resource 01
Chemical Store
Cloaks
Staff & Visitor WC's
Escape Stair
Science Showcase Laboratory
ICT Frame
Sci ICT 01
SS+H Sml 01
SS+H 02
SS+H 03
SS+H 04
SS+H Voc 01
SS+H 01 Showcase
Server Room
WC's
Art 01
Art 02 3D Studio
Kiln
Store
Drama Store
Cleaners Cupboard
Music Ensemble Showcase
Studio 01
Studio 02
Studio 03
Delivery Store
2nd Entrance
Lecture Theatre 01
Lecture Theatre 02
Maths 01 Showcase
Maths 02
Maths 03
Maths 04
AS 01
AS 02
AS 03
AS 04
AS 05
AS 06
AS sml 01
AS sml 02
AS sem 01
AS Discus'n
AS recept'n/ admin
Sick Bay
Coms 01 Showcase
Coms 02
Coms 03
Tech Computing
Tech Engineering
Tech 01 Gen/ICT 01 Showcase
Tech Material Prep & Store 01
Tech Product Design 01
Tech Textiles 01
Recep'n
Academy Community Entrance
Fitness
Change 1
Change 2
Change 3
Change 4
Staff Change
Mat Store
Sports Storage
Chair Store
Electricity switch
Sports Class
Plant
Sports Centre
Kitchen - delivery and storage
WC
6200
A-A A1175
B-B A1175
C-C A1175
D-D A1176
E-E A1176
F-F A1176
G-G A1176
03 A1631
03 A1632
03 A1633
02 A1640
02 A1641
A1820
A1821
A1822
A1823
A1824
A1825
A1826
A1827
A1828
A
B
C
D
E
F
G
H
J
K
L
M
N
1
2
3
4
5
6
7
8
9
10
11
12
13
14
15
16
17
18
19
20
21
22
23
24

General Notes

1. Do not scale drawings. Dimensions govern.
2. All dimensions are in millimetres unless noted otherwise.
3. All dimensions shall be verified on site before proceeding with the work.
4. Foster and Partners shall be notified in writing of any discrepancies.
5. For Building set-out information, refer to A1010, A1011, A1012 & A1013.

Rev.	Date	Reason For Issue	Check
B03	18.09.06	Issued for Information	
B02	27.02.06	Issued for Tender	
B01	15.02.06	Issued for Tender	
A01	31.01.06	Issued for information	

Key Plan

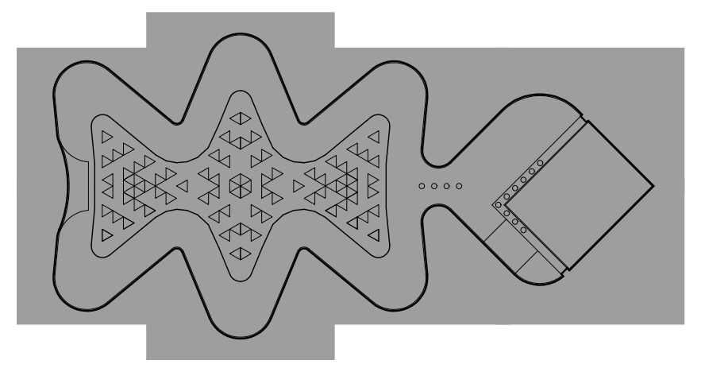

Foster and Partners
architects and designers

Riverside Three
22 Hester Road
London SW11 4AN
Telephone 020 7738 0455
Fax 020 7738 1107 and 1108

Buro Happold
engineers

17 Newman Street
London W1T 1PD
Telephone 020 7927 9700
Fax 020 7927 9701

Davis Langdon
quantity surveyors

Midcity Place
71 High Holborn
London WC1V 6QS
Telephone 020 7061 7000
Fax 020 7061 7061

Project

Thomas Deacon Academy Peterborough

Title

Ground Floor Plan- Furniture & Equipment- FIxed & Loose overview

Job No	Scale	Number
1269	1:200	A1800
Date	**Revision**	
12.01.06	B03	

© Foster and Partners 2003

A0 sheet size

19-SEP-2006 11:10