Lewis & Hickey Ltd, Registered in England & Wales: 2007297 VAT No: 440618076

NOTES

ORIGINAL A1


Lewis & Hickey accept no responsibility for any costs, losses, claims howsoever arising from these drawings, specifications and related documents unless there is full compliance with the client and any authorised user of the following:

1. All boundaries, dimensions and levels are to be checked on site before construction and any discrepancies are to be reported to the Architect / Designer.
2. Partial Service: Any discrepancies with site or other information is to be advised to the Architect / Designer and direction or approval is to be sought before the implementation of the detail.
3. Block and site plans are reproduced under license from the Ordnance Survey.
4. Do not scale this drawing.
5. For the purpose of coordination, all relevant parties must check this information prior to implementation and report any discrepancies to the Architect / Designer.

TENDER


Drawing Issue

Not for construction purposes

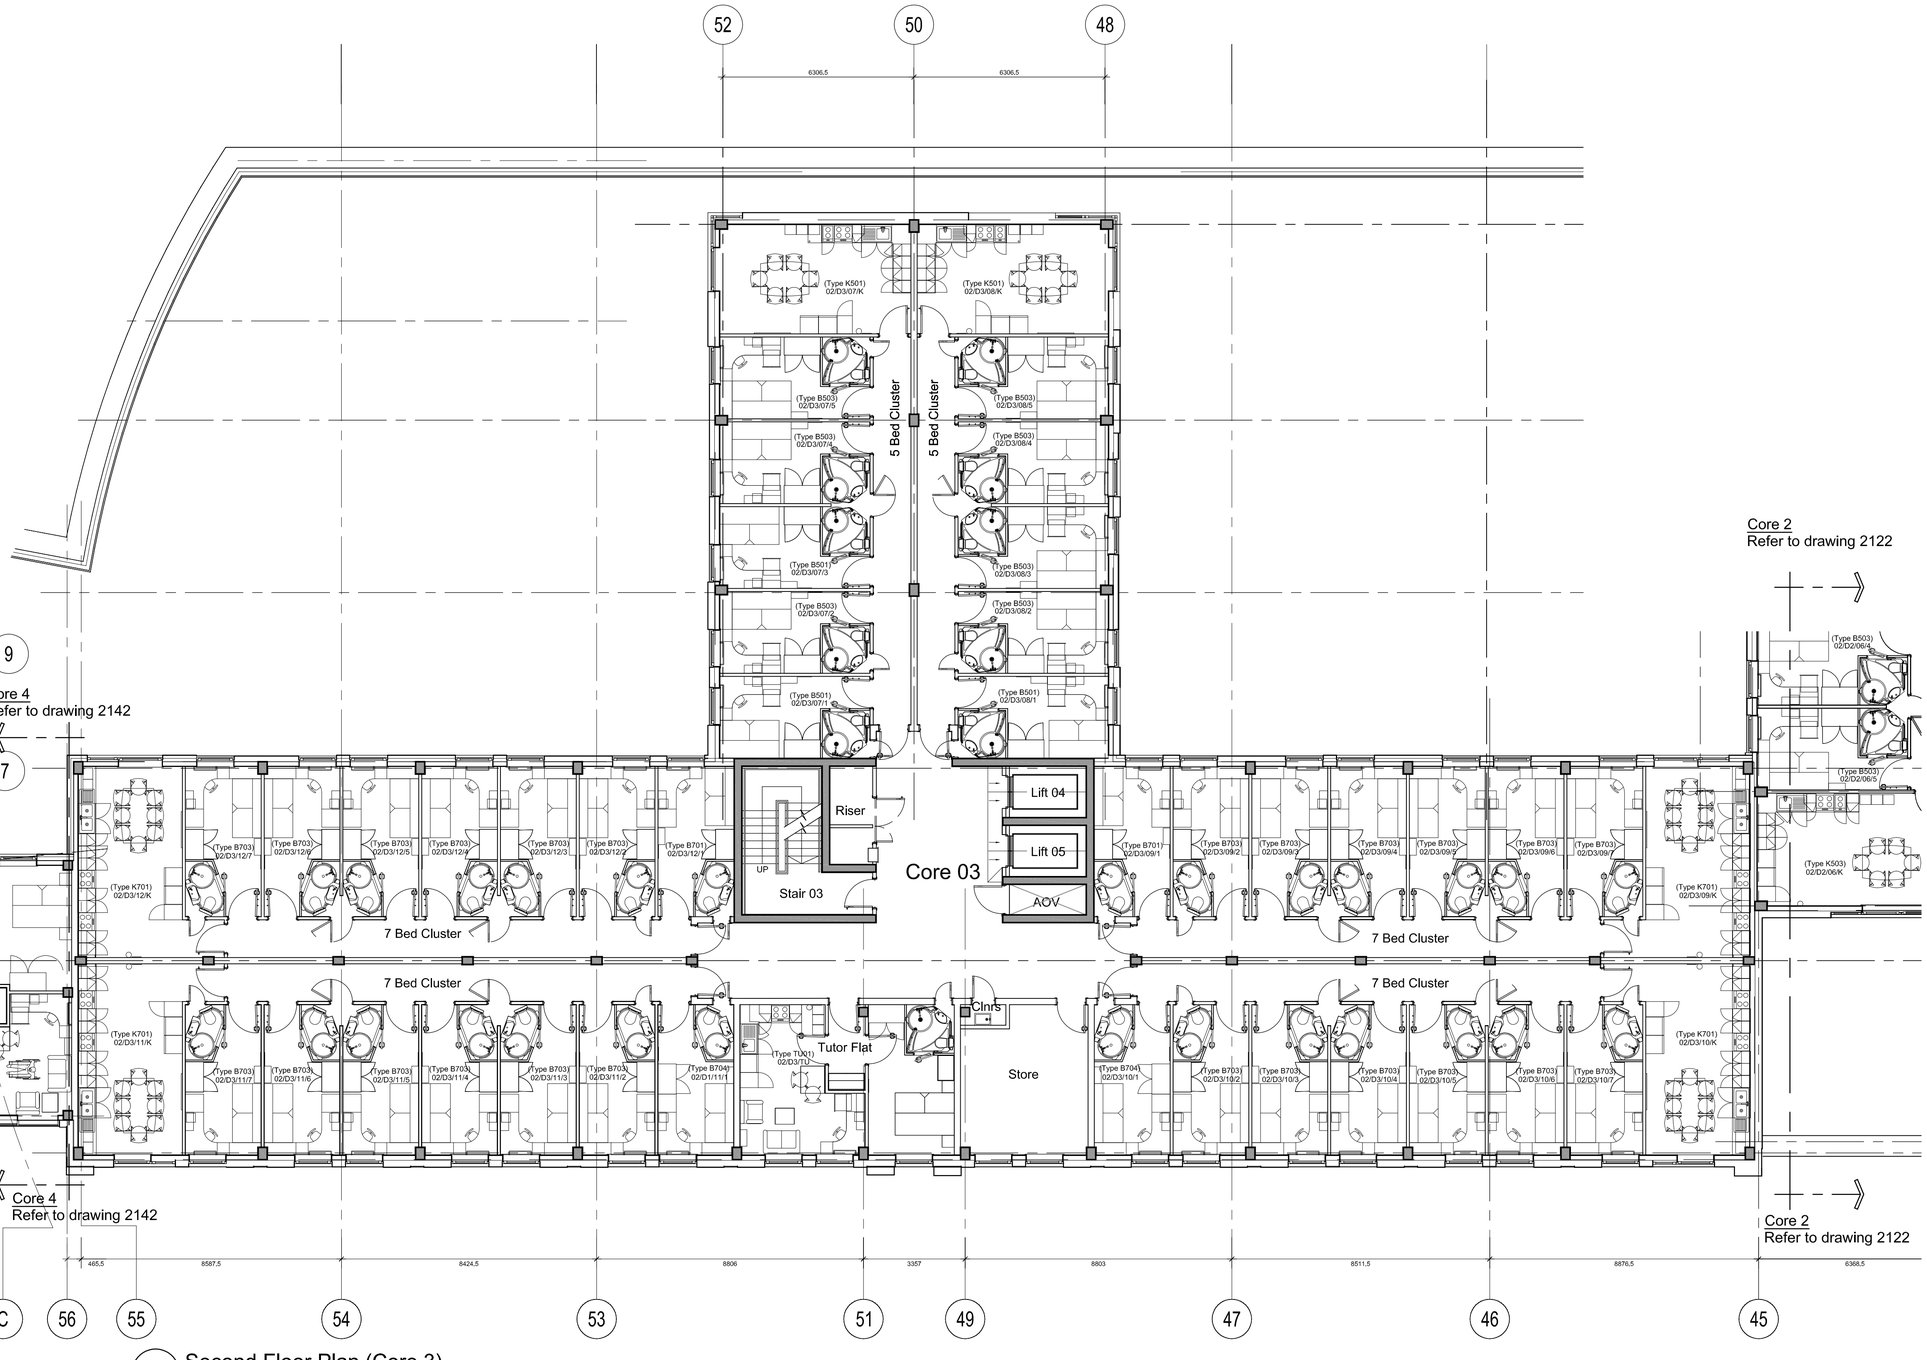

Second Floor Plan (Core 3)

Scale 1:100

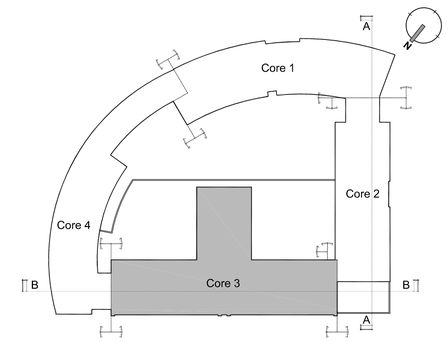

Key Plan

REV	DATE	DESCRIPTION	DRN	CHKD
F	25.06.2010	TV & BRACKET OMITTED AS REQUESTED BY CLIENT.	JH	KS
E	25.05.2010	GAs updated following coordination exercise with consulting engineer. Blockwork shown behind all areas of brick facade as advised by consulting engineer. External set out dimensions transfered to detailed elevation drawings.	JH	KS
D	30.04.2010	GA's revised following structural coordination exercise with BJB. Minor amendments to facade, dimension to suit.	JH	KS
C	23.03.2010	All internal walls aligned to be tangential with SOP Updated Structural Engineers information added. Window type amended. Riser arrangement updated to suit CPW Info.	JK	KS
B	14.01.10	Tender Issue	NLC	KS
A	08.12.2009	Structure integrated into drawing. Minor corrections.	JK	KS

CLIENT

ASTON STUDENT VILLAGES

PROJECT

CAMPUS REDEVELOPMENT
Phase 2 - Block C & D

DRAWING

Block D
Proposed Second Floor Plan 02
Core 3

Hazlemont House
11 Gregory Boulevard
Nottingham, NG7 6LB

Tel: 0115 962 9000
Fax: 0115 962 9001
Email: nottingham@lewishickey.com

SCALE	DATE	DRAWN	CHECKED
1:100	10.11.09	JK	KS
PROJECT No	DRAWING No	STATUS	REV
N5001	2132	T	F

I = Information, T = Tender, C = Construction, R = Record